1 SOUTHWEST 3D View

2 SOUTHEAST 3D View

3 NORTHEAST 3D View

DAN SCOTT DESIGNS
Architectural Services
Architectural Plans - 3D Renderings
DANSCOTTDESIGNS.COM
DAN SCOTT
1548 Back Westminster Rd.
Westminster , Vt. 05158
Email : dscottd @ comcast.net
Phone / Fax
802-463-1961

ROGER SMITH

TREEHOUSE LOG HOMES EAST


DAVID OSTAFIN RESIDENCE
25 HIGGLEY HILL RD
DOVER , Vermont - PRELIMINARY PLAN

Issue Date 1/26/2026
Drawn by DSD
Revised:
Scale

A1

3D Views


1/26/2026 2:43:51 PM

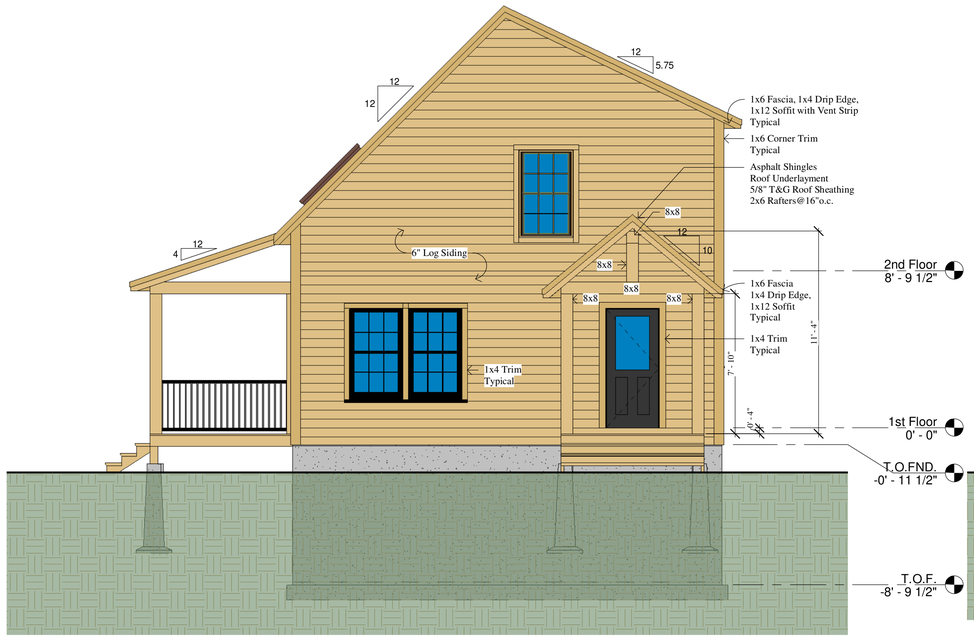

2 EAST ELEVATION
1/4" = 1'-0"



4 SOUTH ELEVATION
1/4" = 1'-0"

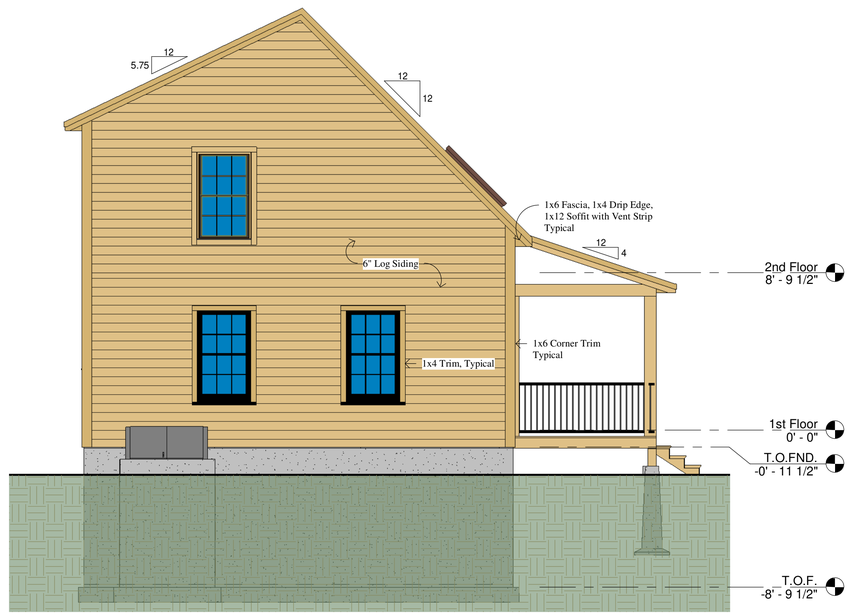

3 WEST ELEVATION
1/4" = 1'-0"



1 NORTH ELEVATION
1/4" = 1'-0"

ROGER SMITH

TREEHOUSE LOG HOMES EAST

DAN SCOTT DESIGNS
Architectural Services
Architectural Plans - 3D Renderings
DANSCOTTDESIGNS.COM
DAN SCOTT
1548 Back Westminster Rd.
Westminster , Vt. 05158
Email : dscottd @ comcast.net
Phone / Fax
802-463-1961

DAVID OSTAFIN RESIDENCE
25 HIGGLEY HILL RD
DOVER , Vermont - PRELIMINARY PLAN

Issue Date 1/26/2026
Drawn by DSD
Revised:
Scale 1/4" = 1'-0"

A2

Elevations

1/26/2026 2:43:53 PM

Door Schedule


Type Mark	Count	Manufacturer	Model	Description	Rough Width	Rough Height
4'	3			4'0 x 6'8 Bi-Fold Door		
30	7			30" x 80"	2' - 9"	6' - 10 1/2"
32	1			36" x 80"	3' - 3"	6' - 10 1/2"
A	1	Therma-Tru	FC65	3'0 x 6'8 Half Light Door	3' - 2 1/2"	6' - 10 1/2"
B	1	Therma-Tru		Full Lite Door	3' - 2 1/2"	6' - 10 1/2"

Window Schedule

Type Mark	Count	Manufacturer	Model	Description	Rough Width	Rough Height
A	10	Andersen	TW210410	Double Hung	3' - 0 1/8"	5' - 0 7/8"
B	1	Andersen	CN235	Double Casement	2' - 10 1/4"	3' - 5 3/8"
C	2	Andersen	TW2036	2036 D.H.	2' - 2 1/8"	3' - 0 7/8"
D	6	Velux	M04	Fix Skylight	2' - 6 1/16"	4' - 6 7/16"




8 3D View of Bedroom 2

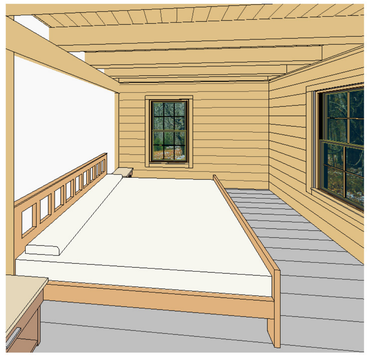

6 3D View of Bedroom 1



5 3D View Loft 2

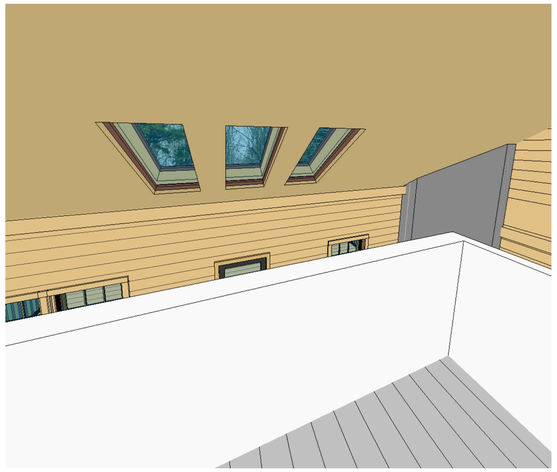


7 3D View Loft 1




4 Great Room 3D View 2



3 Great Room 3D View 1

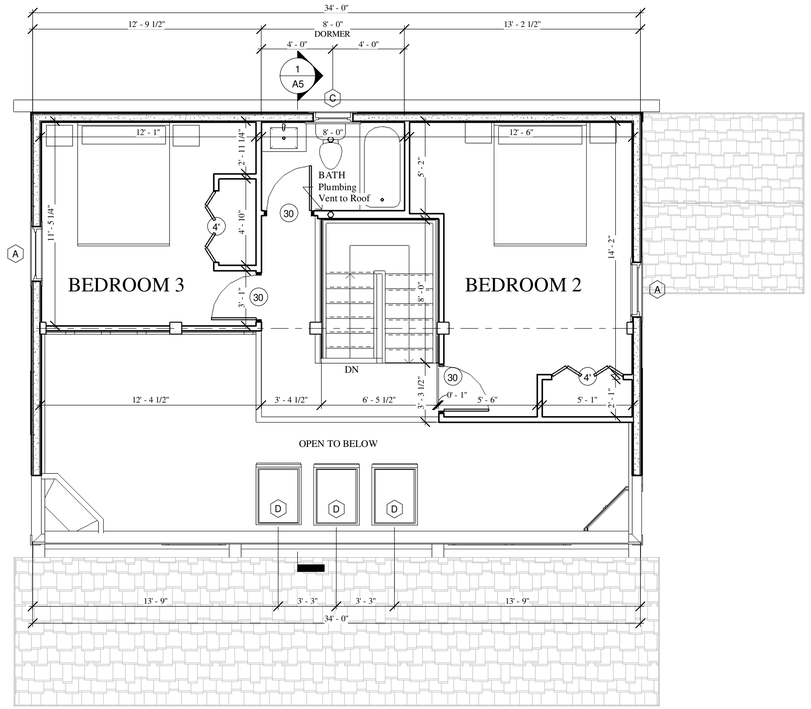

2 2nd Floor
1/4" = 1'-0"

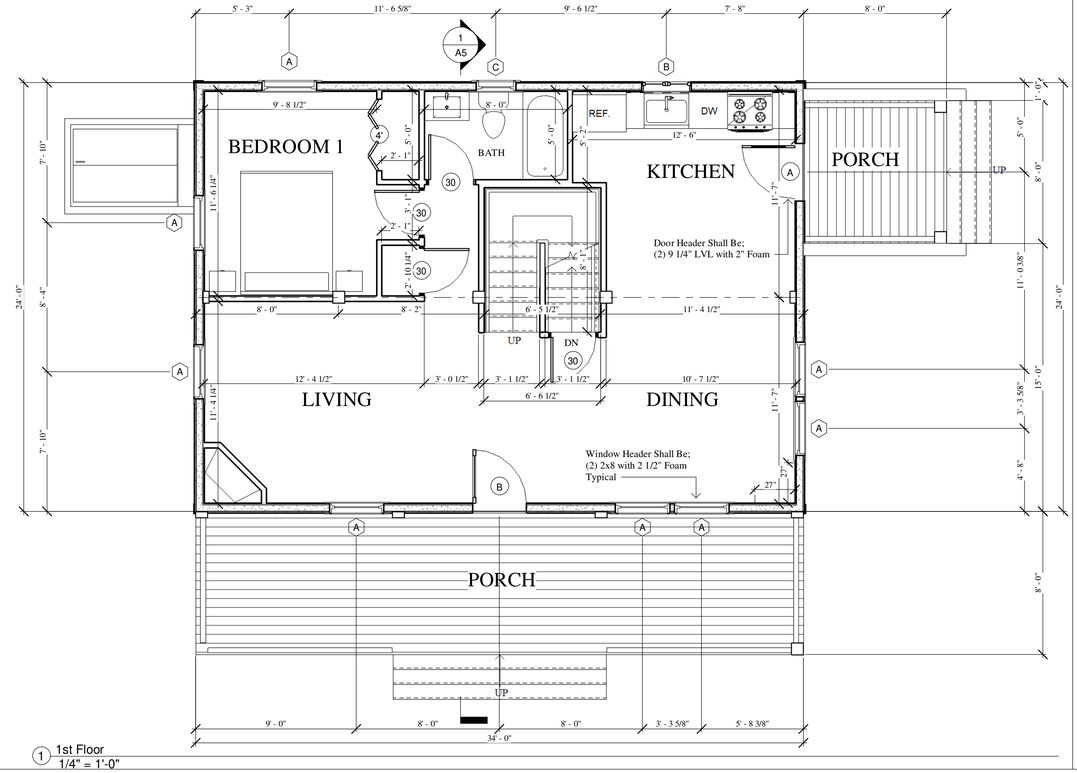

1 1st Floor
1/4" = 1'-0"

DAN SCOTT DESIGNS
Architectural Services
Architectural Plans - 3D Renderings
DANSCOTTDESIGNS.COM

DAN SCOTT
1548 Back Westminster Rd.
Westminster , Vt. 05158
Email : dscottd @ comcast.net
Phone / Fax
802-463-1961

ROGER SMITH
TREEHOUSE LOG HOMES EAST


DAVID OSTAFIN RESIDENCE
25 HIGGLEY HILL RD
DOVER , Vermont - PRELIMINARY PLAN

Issue Date 1/26/2026
Drawn by DSD
Revised:
Scale 1/4" = 1'-0"


A3

1st & 2nd Floor Plans


1/26/2026 2:44:03 PM

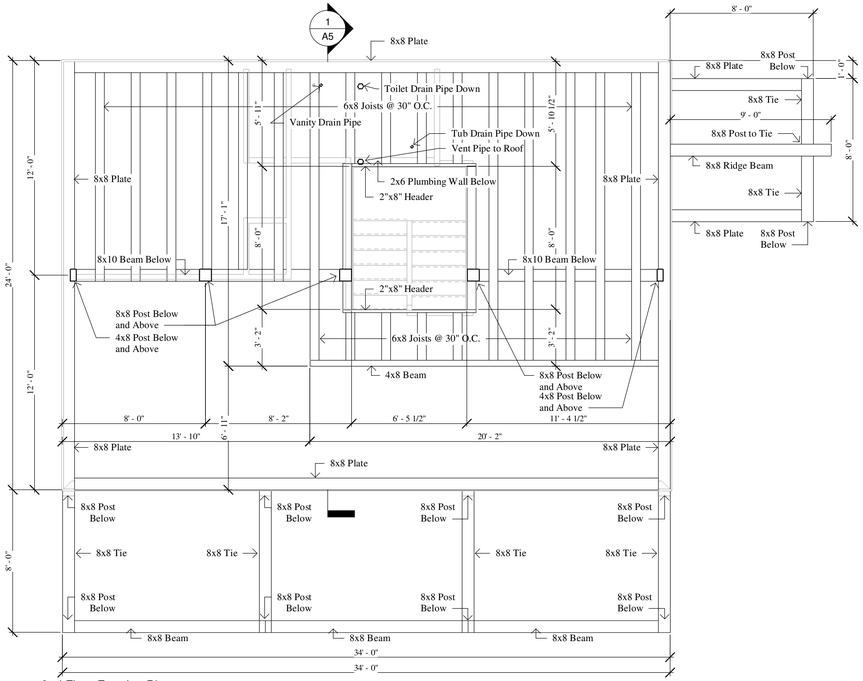


3 2nd Floor Framing Plan
1/4" = 1'-0"

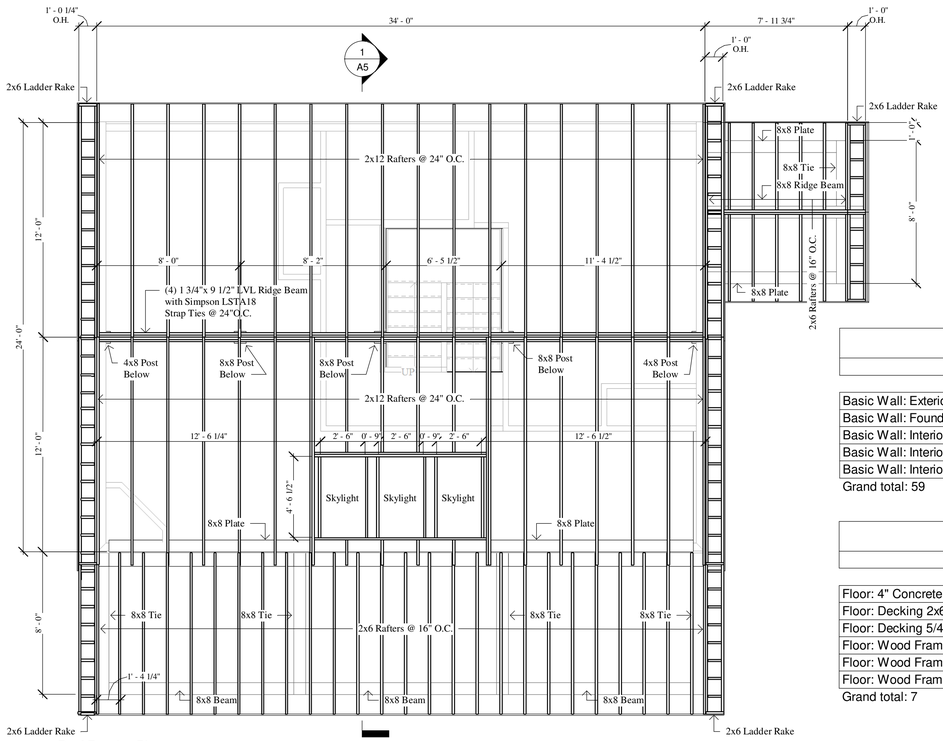

4 Roof Framing Plan
1/4" = 1'-0"

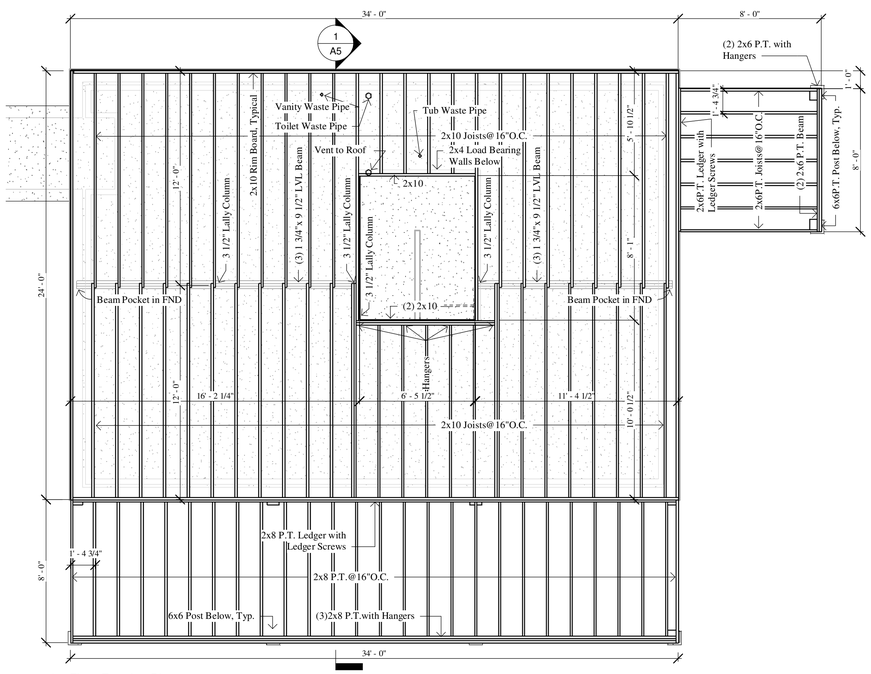

2 1st Floor Framing Plan
1/4" = 1'-0"

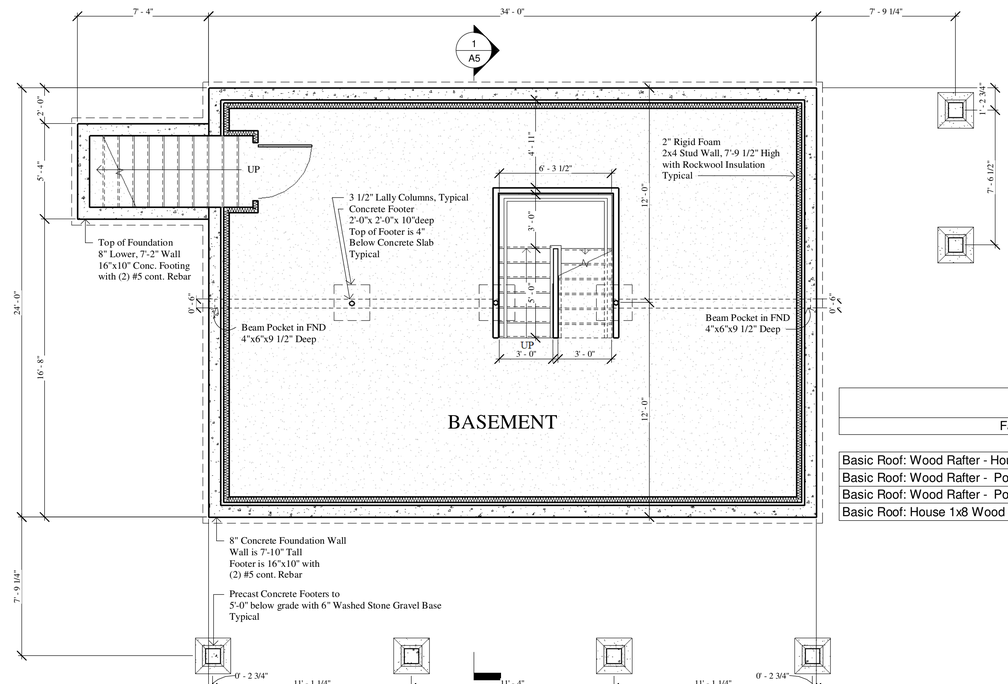

1 Basement Plan
1/4" = 1'-0"

Structural Foundation Schedule		
Family and Type	Length	Volume
Wall Foundation: Retaining Footing - 16"x10"	128' - 0"	142.22 CF
Grand total: 8	128' - 0"	142.22 CF

Wall Schedule		
Family and Type	Area	Volume
Basic Wall: Exterior - 5" Sip & Log Siding	1697 SF	828.64 CF
Basic Wall: Foundation - 8" Concrete	990 SF	660.15 CF
Basic Wall: Interior - 3 1/2" Partition with Sheetrock	2338 SF	681.20 CF
Basic Wall: Interior - 3 1/2" Partition with Stone Facade	64 SF	16.64 CF
Basic Wall: Interior - 5 1/2" Partition with Sheetrock	91 SF	41.28 CF
Grand total: 59	5180 SF	2227.92 CF

Floor Schedule		
Family and Type	Area	Volume
Floor: 4" Concrete Slab	855 SF	285.04 CF
Floor: Decking 2x6 T&G 2nd Floor Horz	466 SF	63.15 CF
Floor: Decking 5/4 Azek Entry Porch	336 SF	28.00 CF
Floor: Wood Frame 2x6 Entry Porch	64 SF	29.33 CF
Floor: Wood Frame 2x8 Entry Porch	272 SF	164.33 CF
Floor: Wood Frame 2x10 House	764 SF	644.59 CF
Grand total: 7	2757 SF	1214.44 CF

Roof Schedule	
Family and Type	Area
Basic Roof: Wood Rafter - House Roof - Asphalt Shingles	1163 SF
Basic Roof: Wood Rafter - Porch Asphalt Roofing and 1x8 Wood Ceiling	314 SF
Basic Roof: Wood Rafter - Porch Asphalt Roofing and 1x8 Wood Ceiling	118 SF
Basic Roof: House 1x8 Wood Ceiling with 1 1/2" Foil Face ISO. Insul.	944 SF

ROGER SMITH

TREEHOUSE LOG HOMES EAST

DAN SCOTT DESIGNS
Architectural Services
Architectural Plans - 3D Renderings
DANSCOTTDESIGNS.COM
DAN SCOTT
1548 Back Westminster Rd.
Westminster, Vt. 05158
Email : dscottd @ comcast.net
Phone / Fax
802-463-1961


DAVID OSTAFIN RESIDENCE
25 HIGGLEY HILL RD
DOVER , Vermont - PRELIMINARY PLANS

Issue Date	1/26/2026
Drawn by	DSD
Revised:	
Scale	1/4" = 1'-0"

A4

Construction Plans

1/26/2026 2:44:04 PM

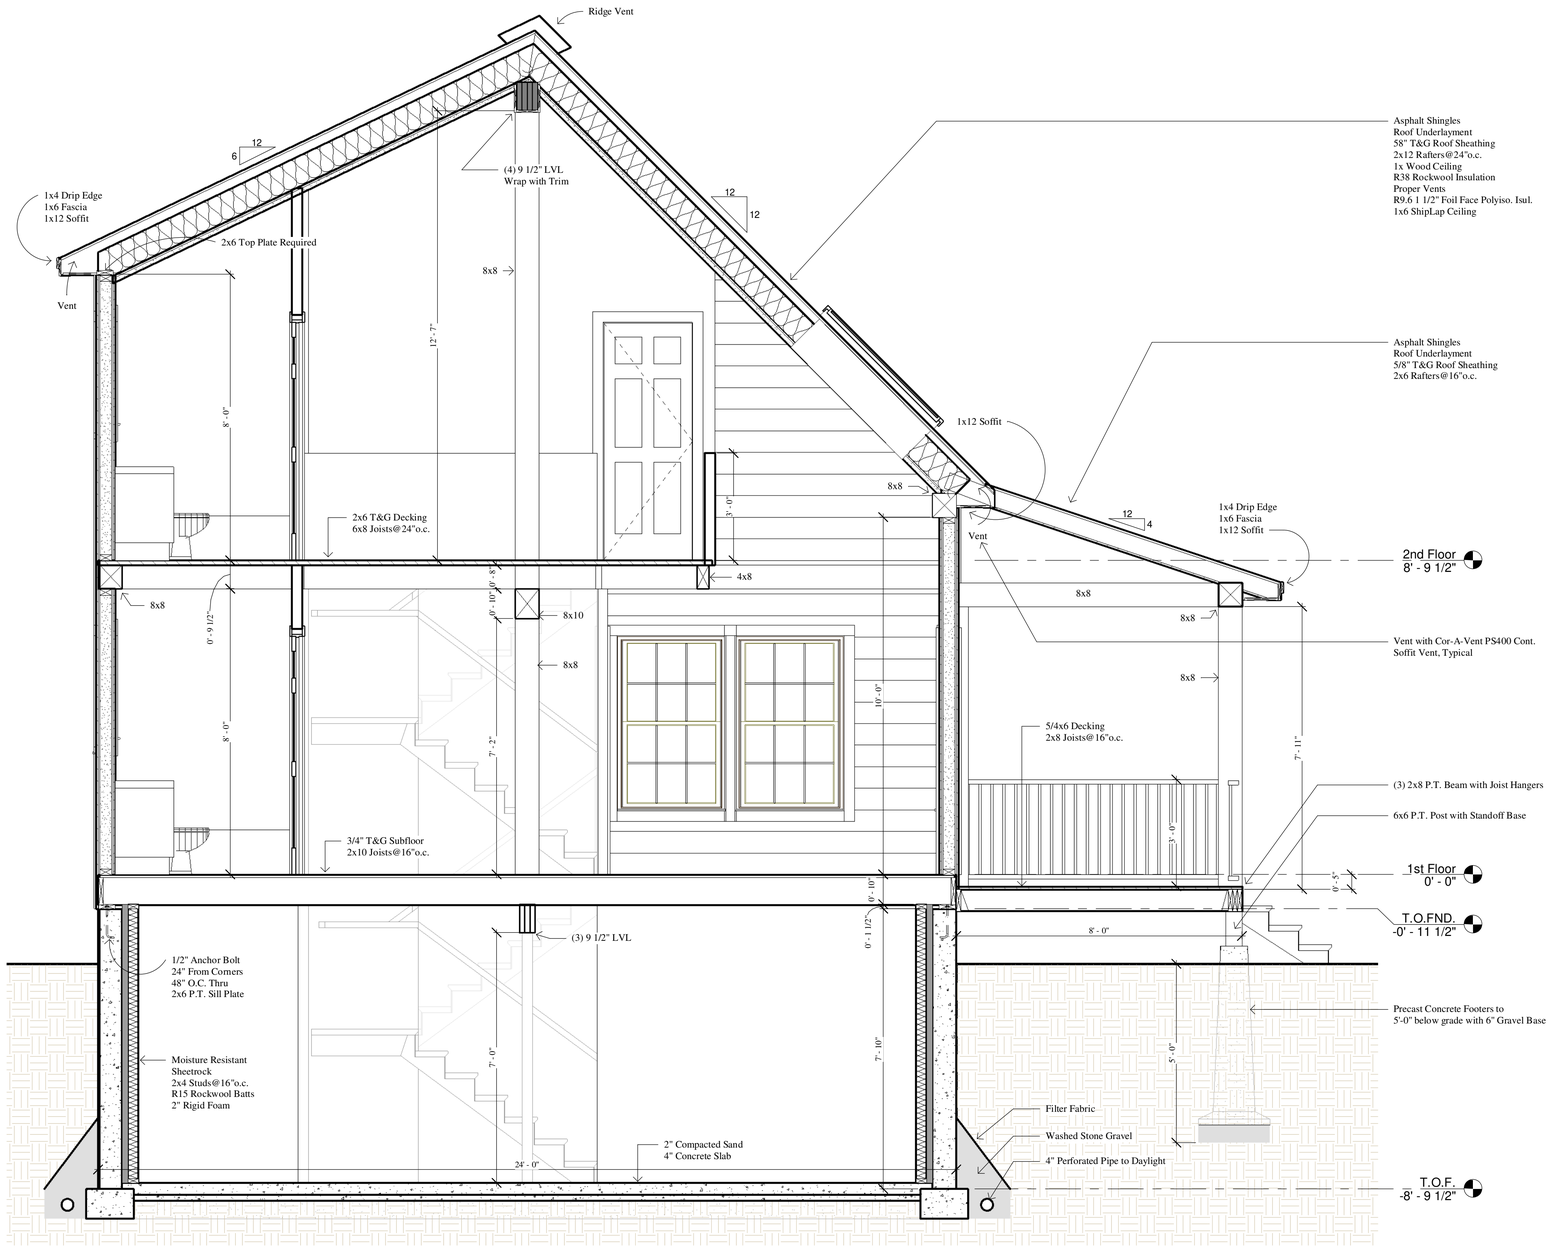

1 Section 1
1/2" = 1'-0"

ROGER SMITH

TREEHOUSE LOG HOMES EAST

DAN SCOTT DESIGNS
Architectural Services
Architectural Plans - 3D Renderings
DANSCOTTDESIGNS.COM
DAN SCOTT
1548 Back Westminster Rd.
Westminster , Vt. 05158
Email : dscottd@ comcast.net
Phone / Fax
802-463-1961

DAVID OSTAFIN RESIDENCE
25 HIGGLEY HILL RD
DOVER , Vermont - PRELIMINARY PLAN

Issue Date	1/26/2026
Drawn by	DSD
Revised :	
Scale	1/2" = 1'-0"

A5

Construction Sections

1/26/2026 2:44:05 PM